

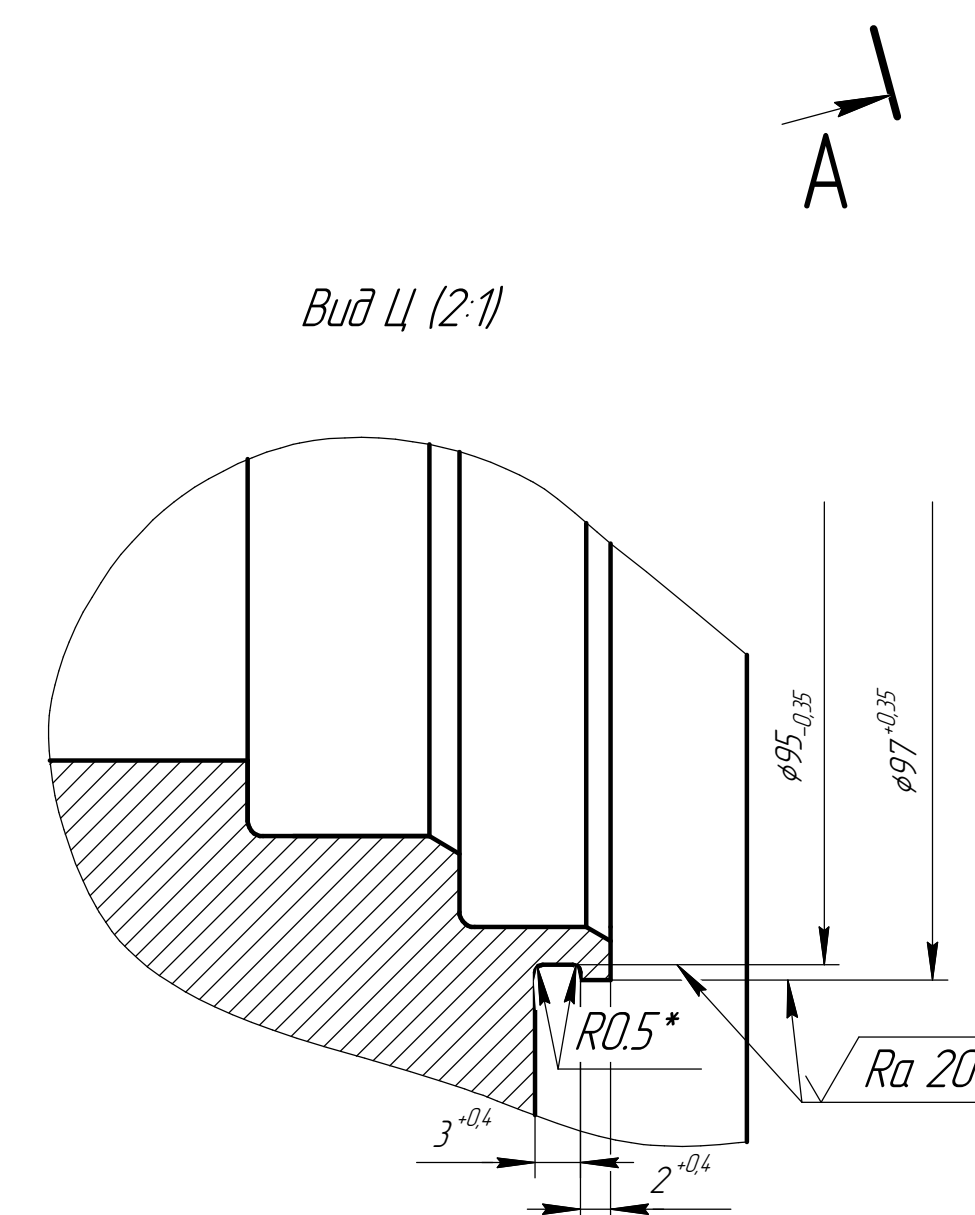
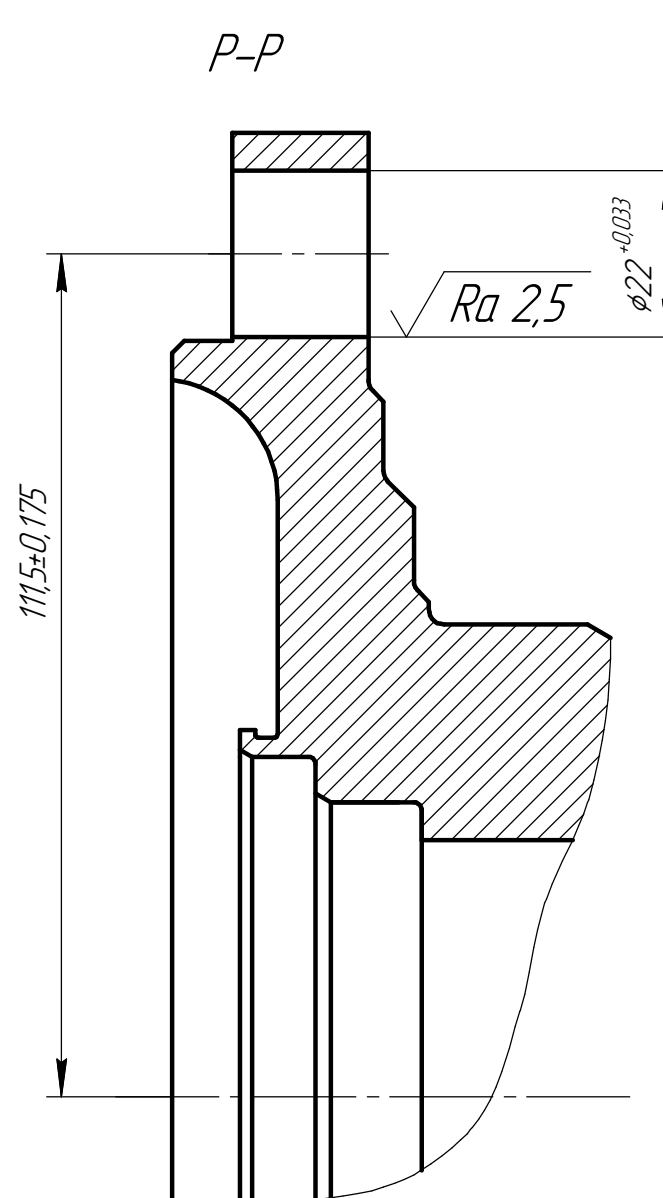


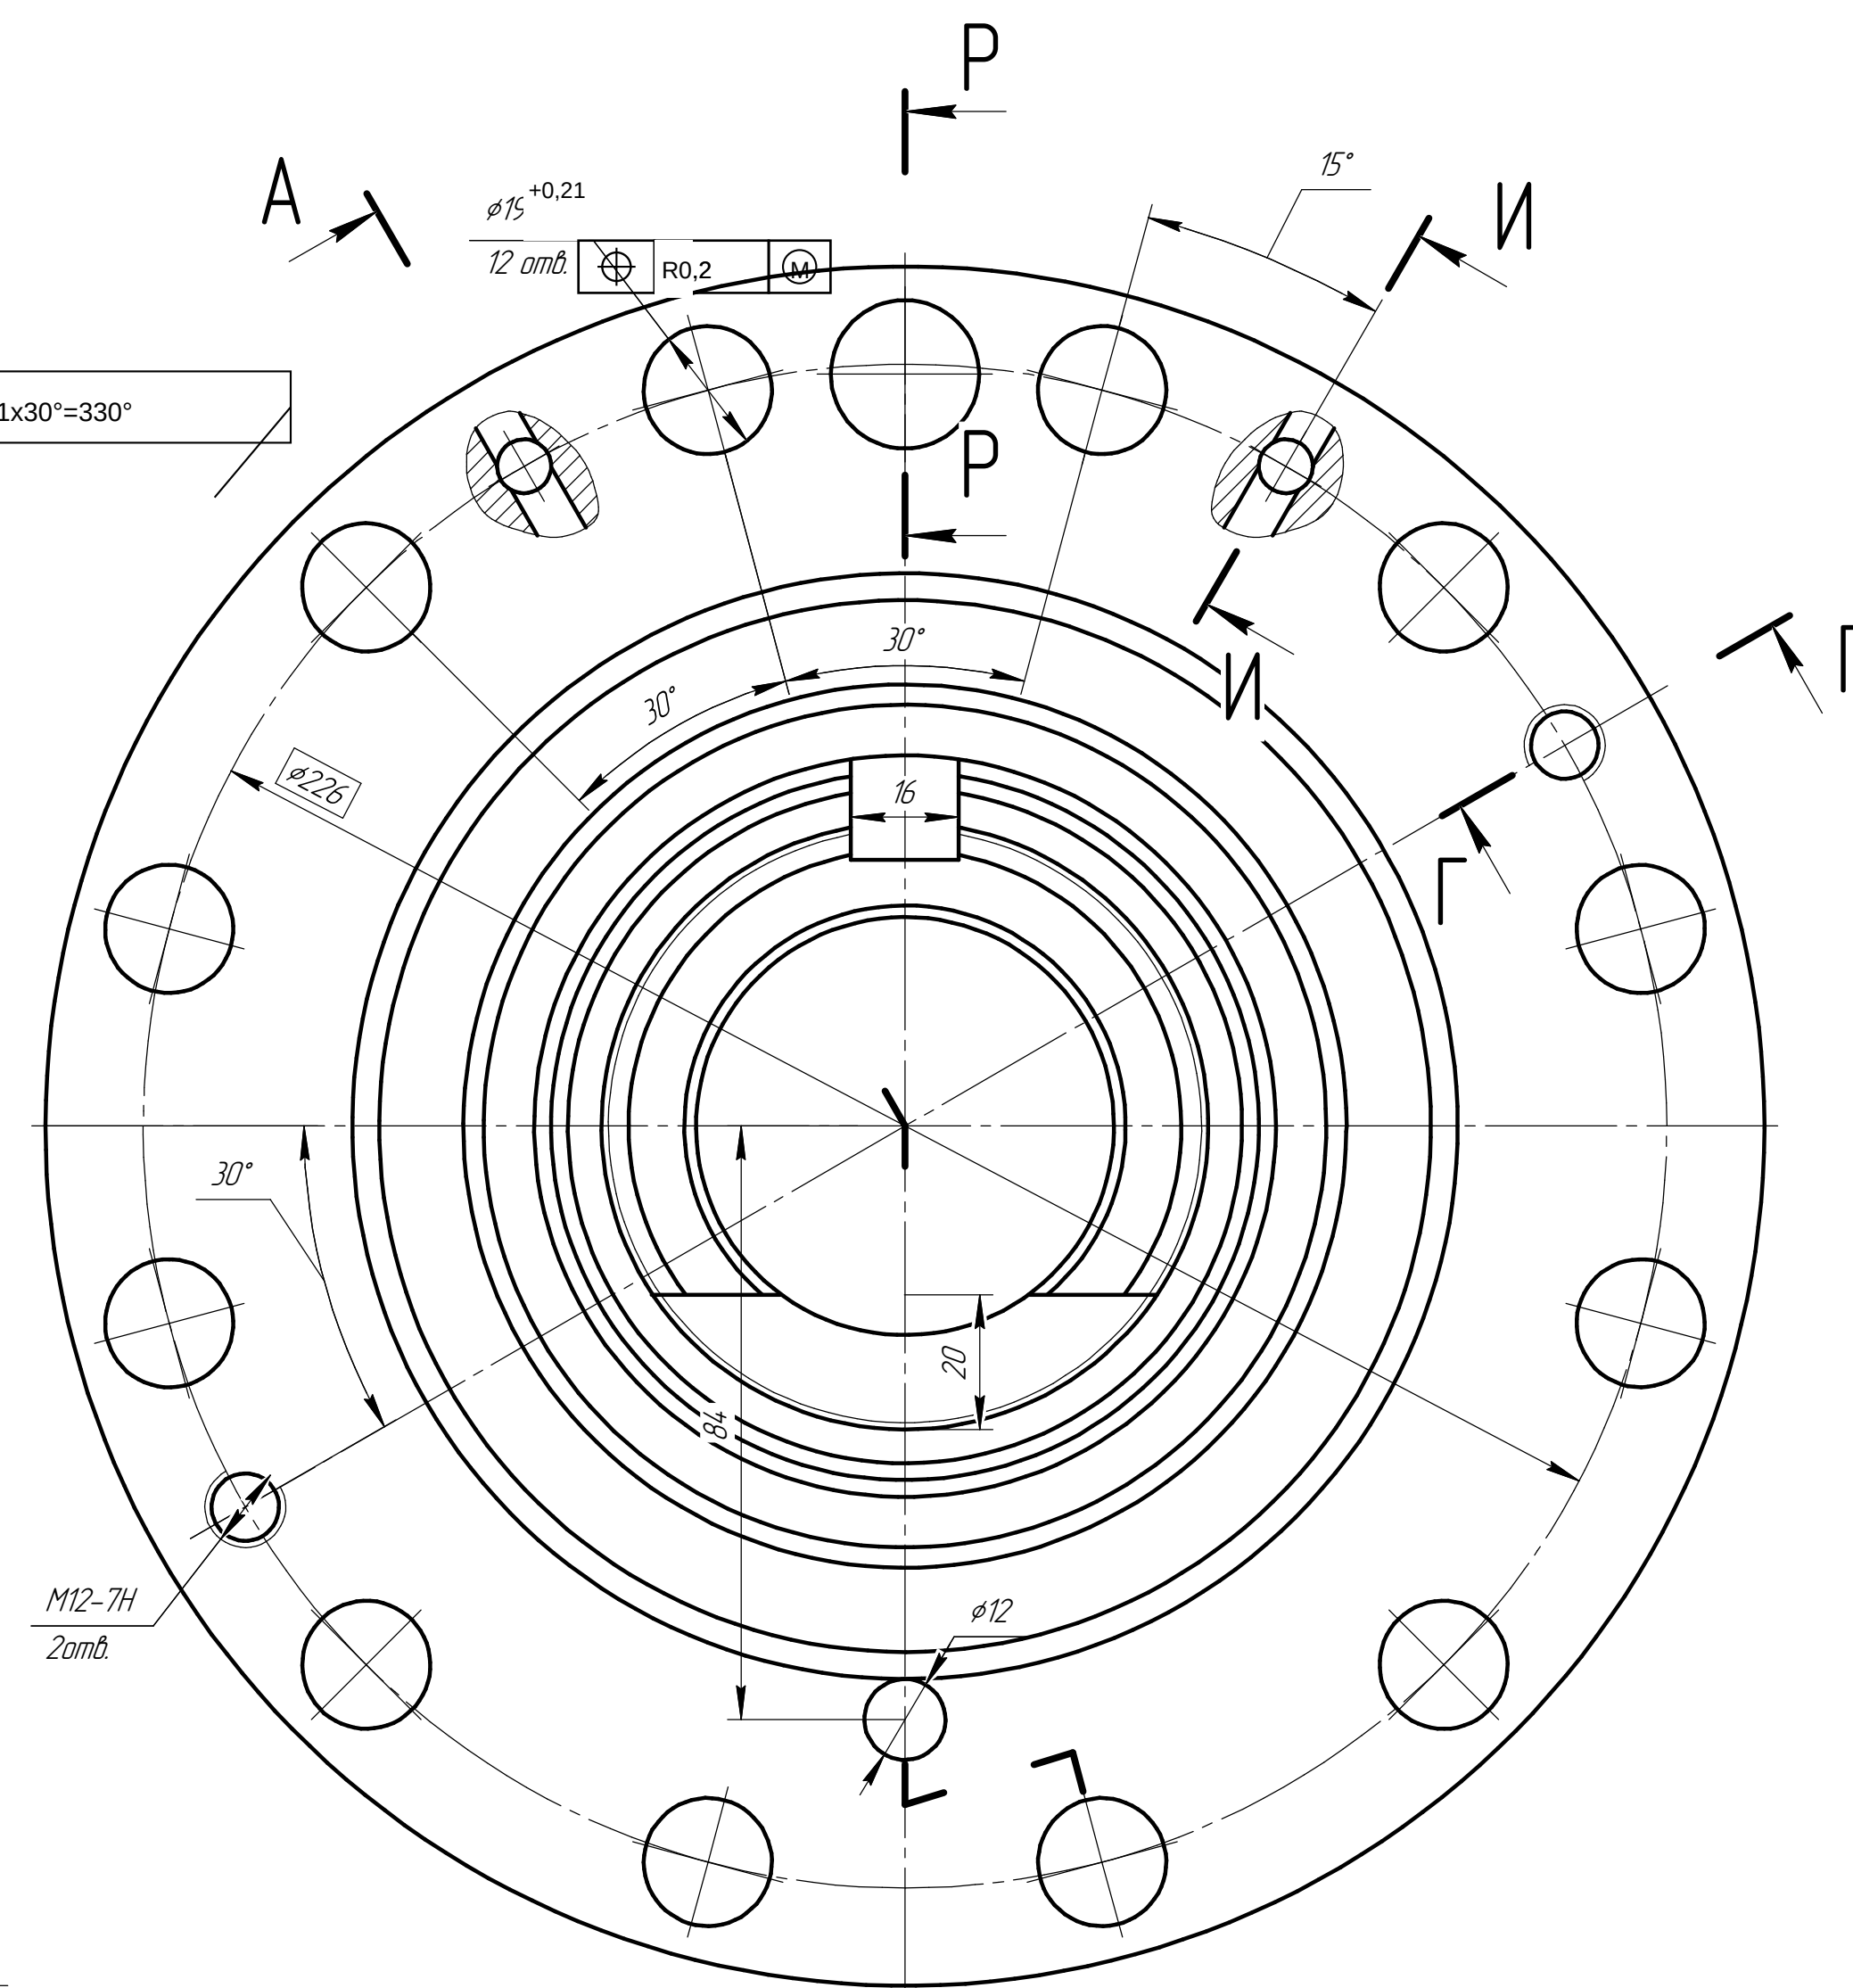

1. 241..285 HB.
2. Общие допуски по ГОСТ 30893.1 H14, h14, $\pm IT14/2$.
3. Допуск непостоянства диаметров в поперечном и продольном сечениях поверхностей М и Ж не более 0.011мм, Н-не более 0.006мм.
4. Допускается ступенчатое уменьшение отверстия Щ и отверстия С на участке У до размера $\phi 6$ мм.
5. Проверить герметичность давлением воздуха 0.6 МПа. При подаче воздуха в канал Э при закрытом отверстии Ш утечка воздуха не допускается.
6. Покрытие поверхностей на участке Я : Х 9 тв. ГОСТ 9.306-85. Допускается наличие хрома на участках Ю.
7. На участке П допускается уменьшение диаметра до размера $\phi 99.5_{-0.021}^{+0.021}$ мм.
8. Прокли поз.3, 5 устанавливать на универсальный герметик УГ-9 ГУ 2257-407-00208947-2004 или УГ-11 ГУ 2257-352-00208947-2001.
9. * Размеры одеспеч. инстр.
10. ** Размер и шероховатость поверхности Ф после покрытия и окончательной обработки.
11. Остальные ТТ по СТБ 1014-95.

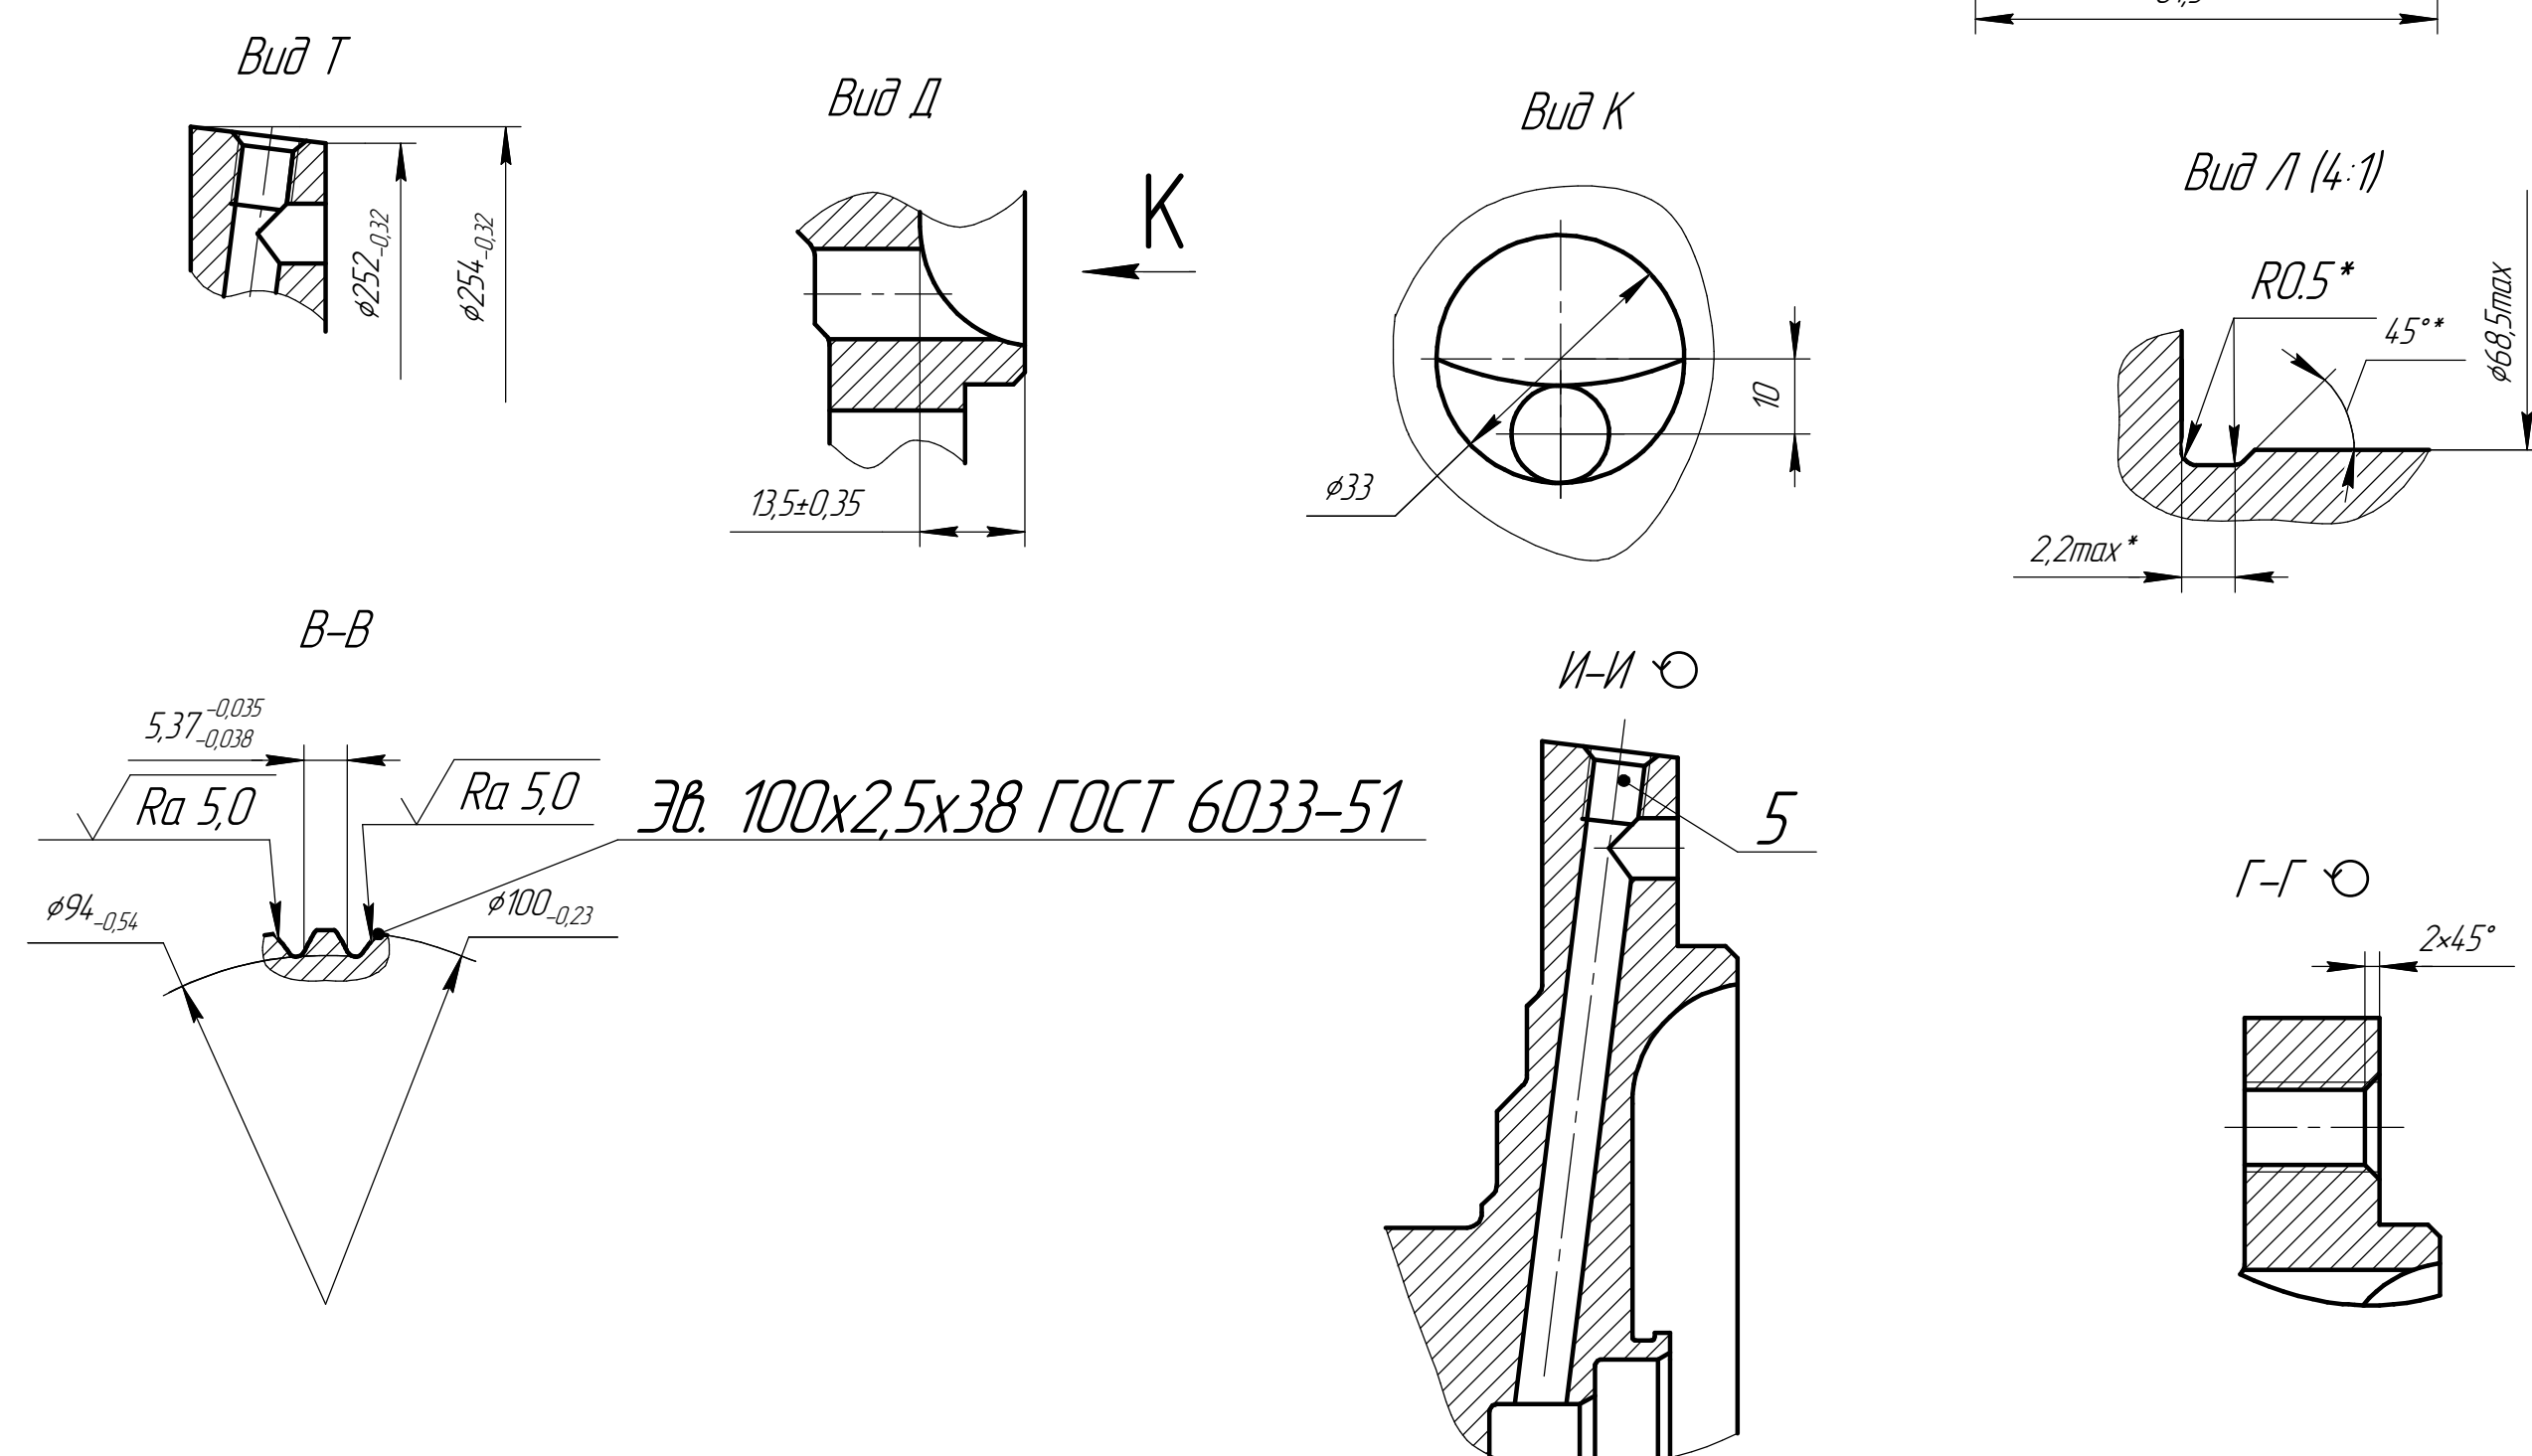

					КП ТМ-36010106.01.00.000-ДО-2021			
Изм	Лист	№ докум.	Подп.	Дата	Цанфа	Лист	Масса	Масштаб
Разраб.		Короткевич А.А.					11,3	1:1
Проб.		Брытик Е.В.						
Т. контр.						Лист	Листов	1
Н.контр.					Сталь 30ХГСА ГОСТ 4543-71	2р 18-ТМ		
Умб.								